

A


B

C

D

E

F

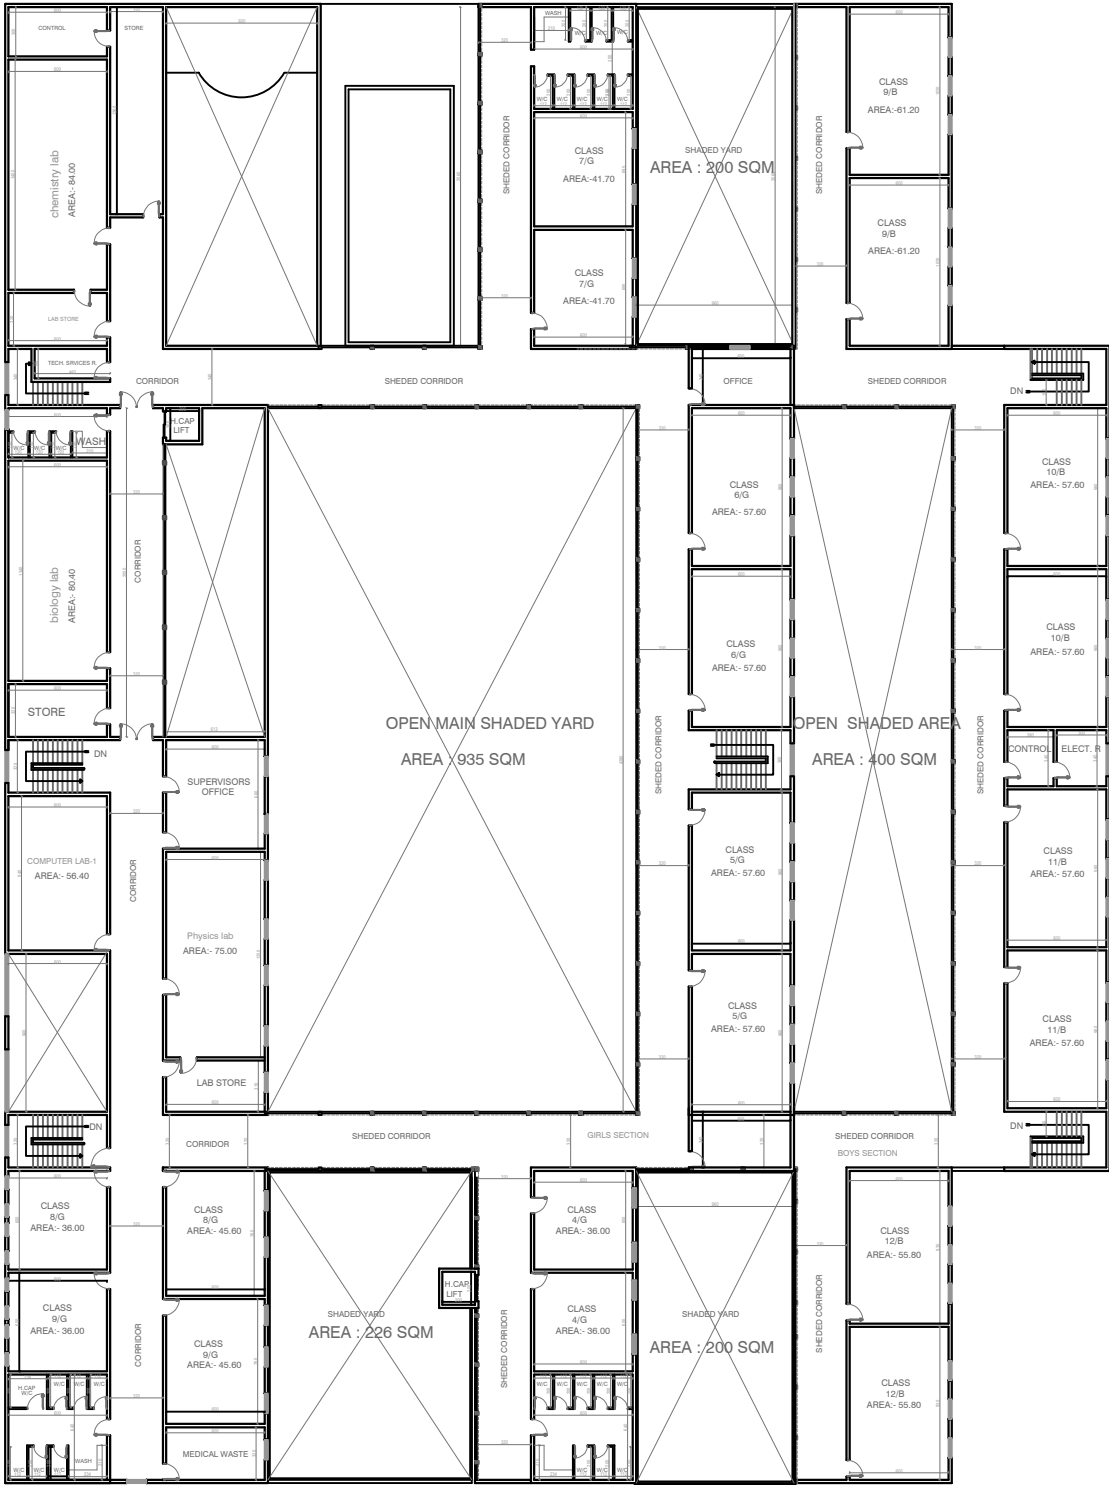

FIRST FLOOR PLAN

HEC **CONSULTANTS** **للإستشارات الهندسية**
AL HES ENGINEERING CONSULTANTS

PHONE : + 971 - 7 - 2260662 P.O. BOX : 33329 , R.A.K , U.A.E.
FAX : + 971 - 7 - 2260671 E - MAIL : 000000000000000000

Client	Al-Nasr Model Private School		
Project	BRANCH-2		
Drg.Title	FIRST FLOOR PLAN		
Area	DAHAN	Floortype	
Case ID.		Draw. Type	ARCH
Sec No.		Com. No.	
Block No.	60	Plot No.	314044020
Bldg. No.		Floor No.	
Date	MAY 2026	Sht. No.	A03
Scale	1:100	Job No.	
G.Manager	Architect	Drawn by	
M.ALI	SHUTTY	SHUTTY	